




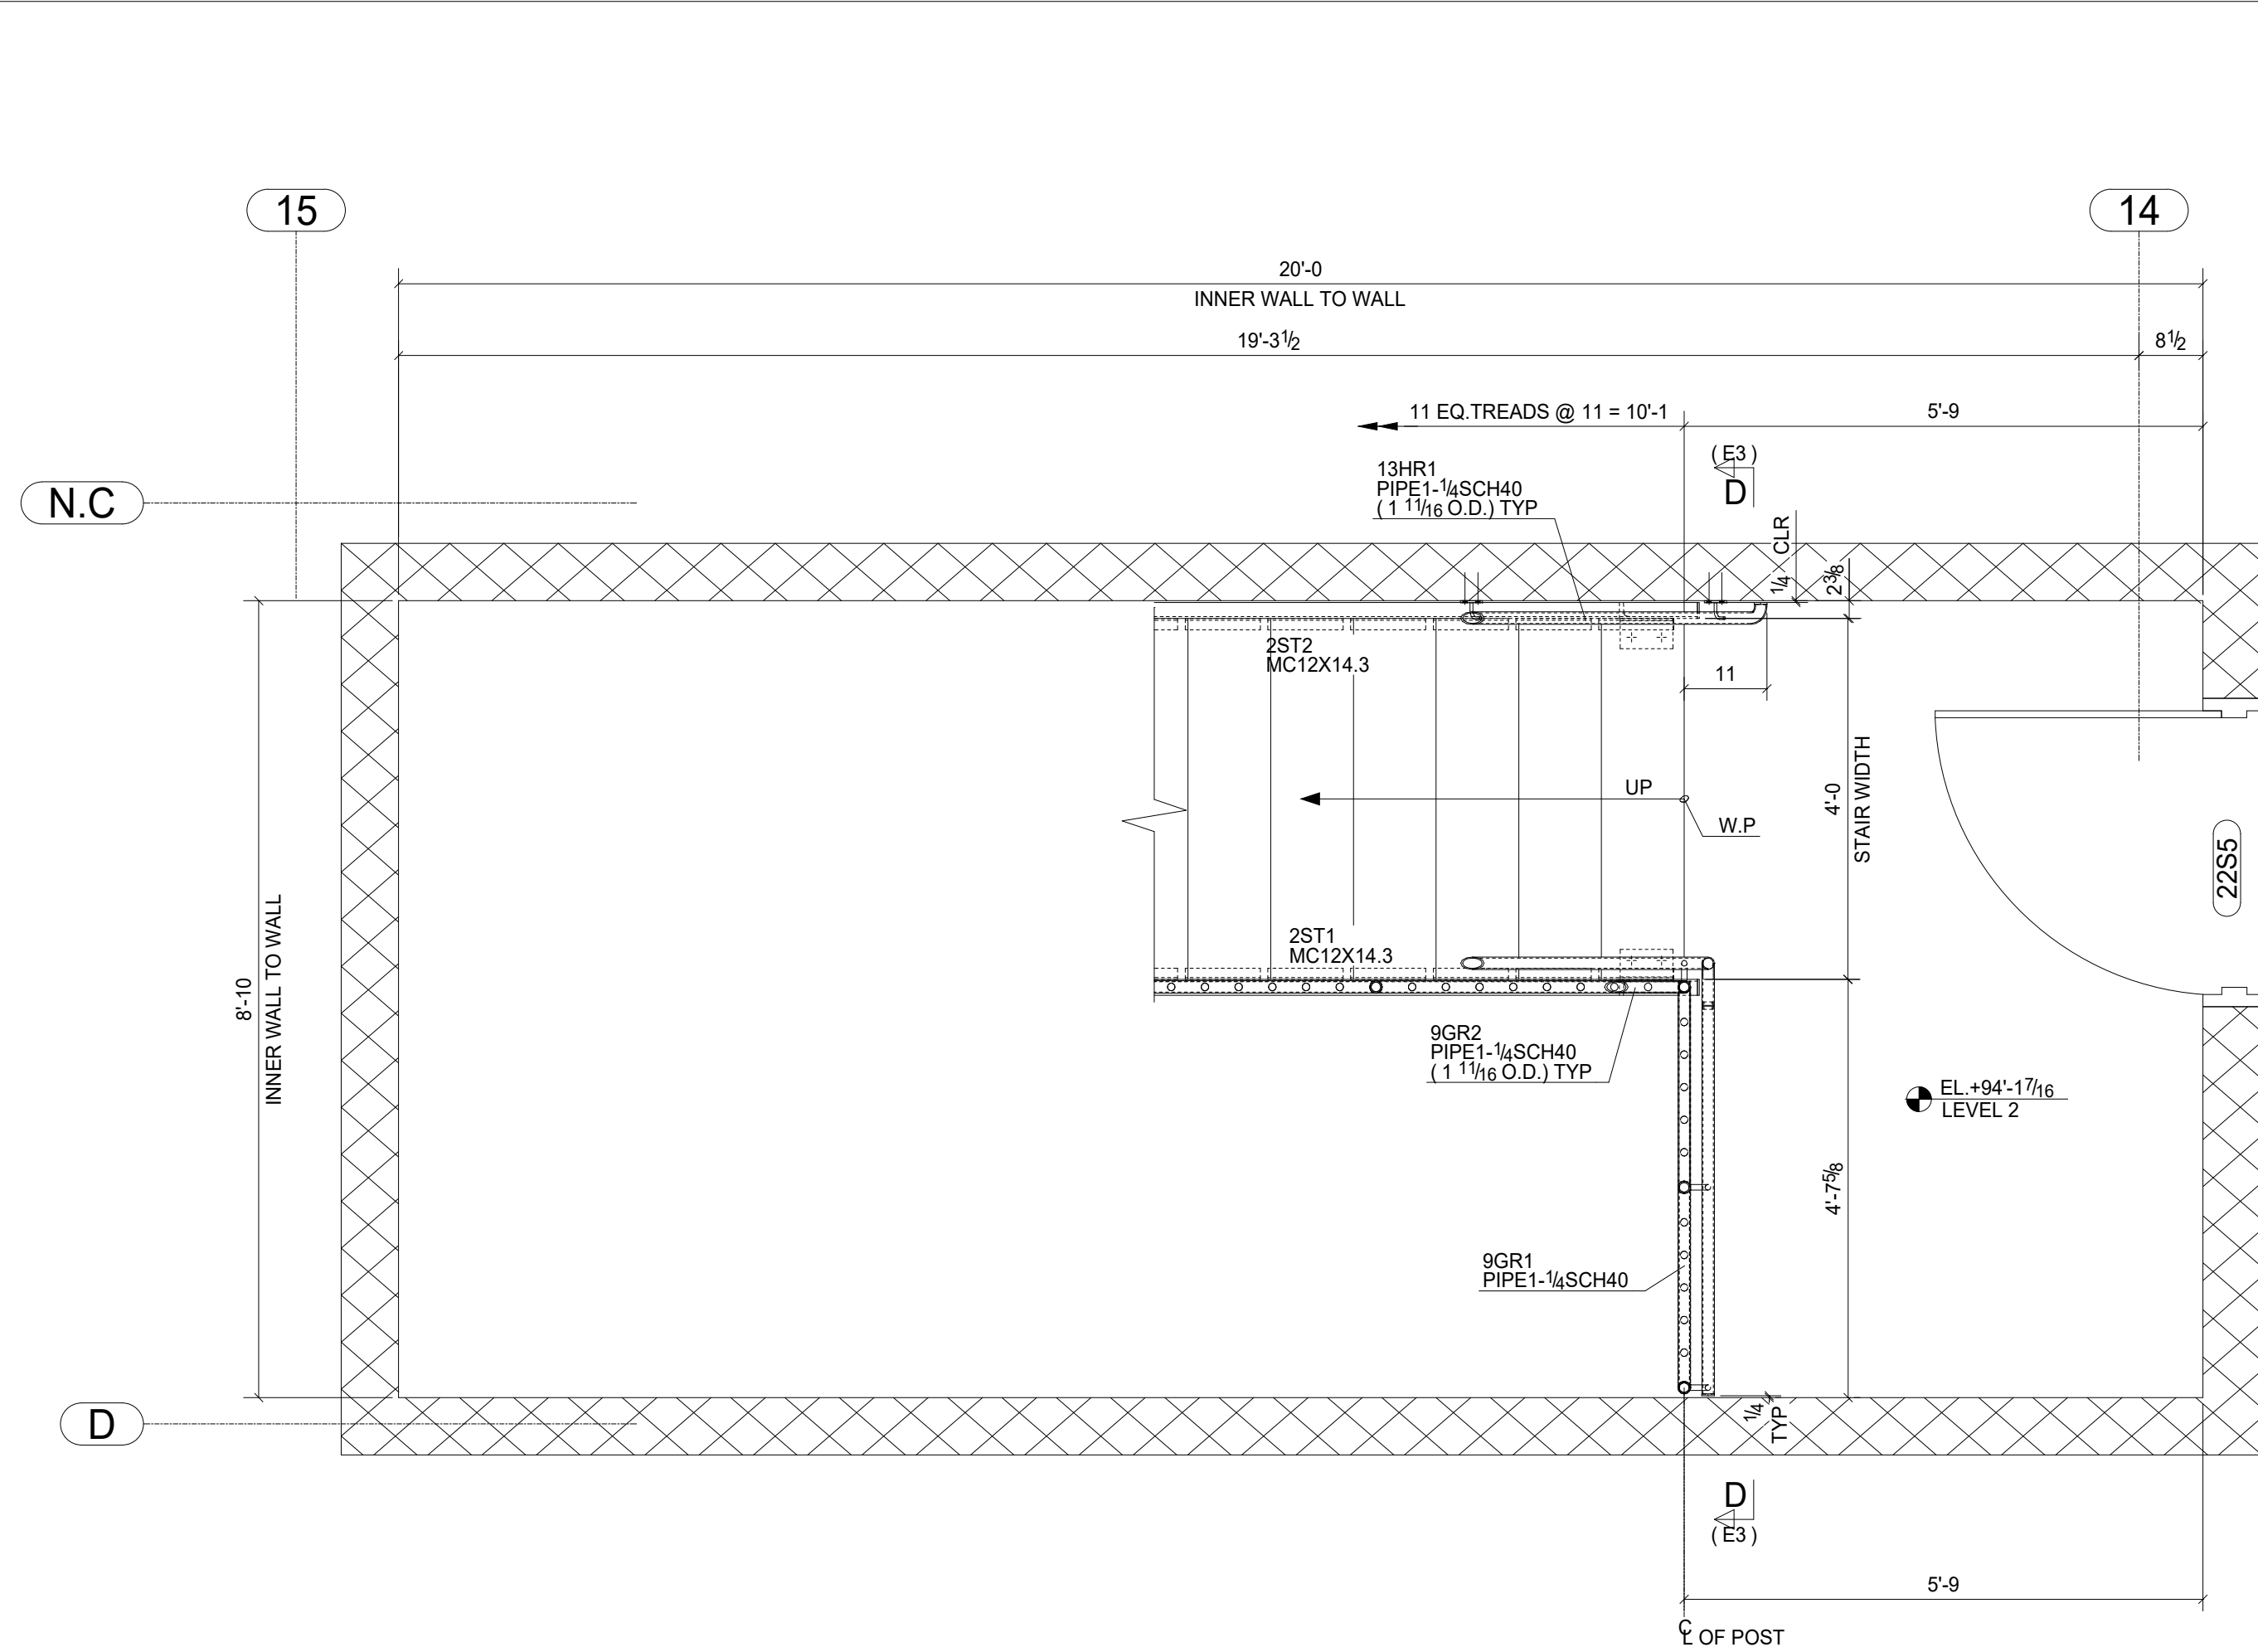

STAIR 1 MARKING PLAN AT LEVEL 1
(REF. CONTRACT DWG. NO. - 1/A0860)

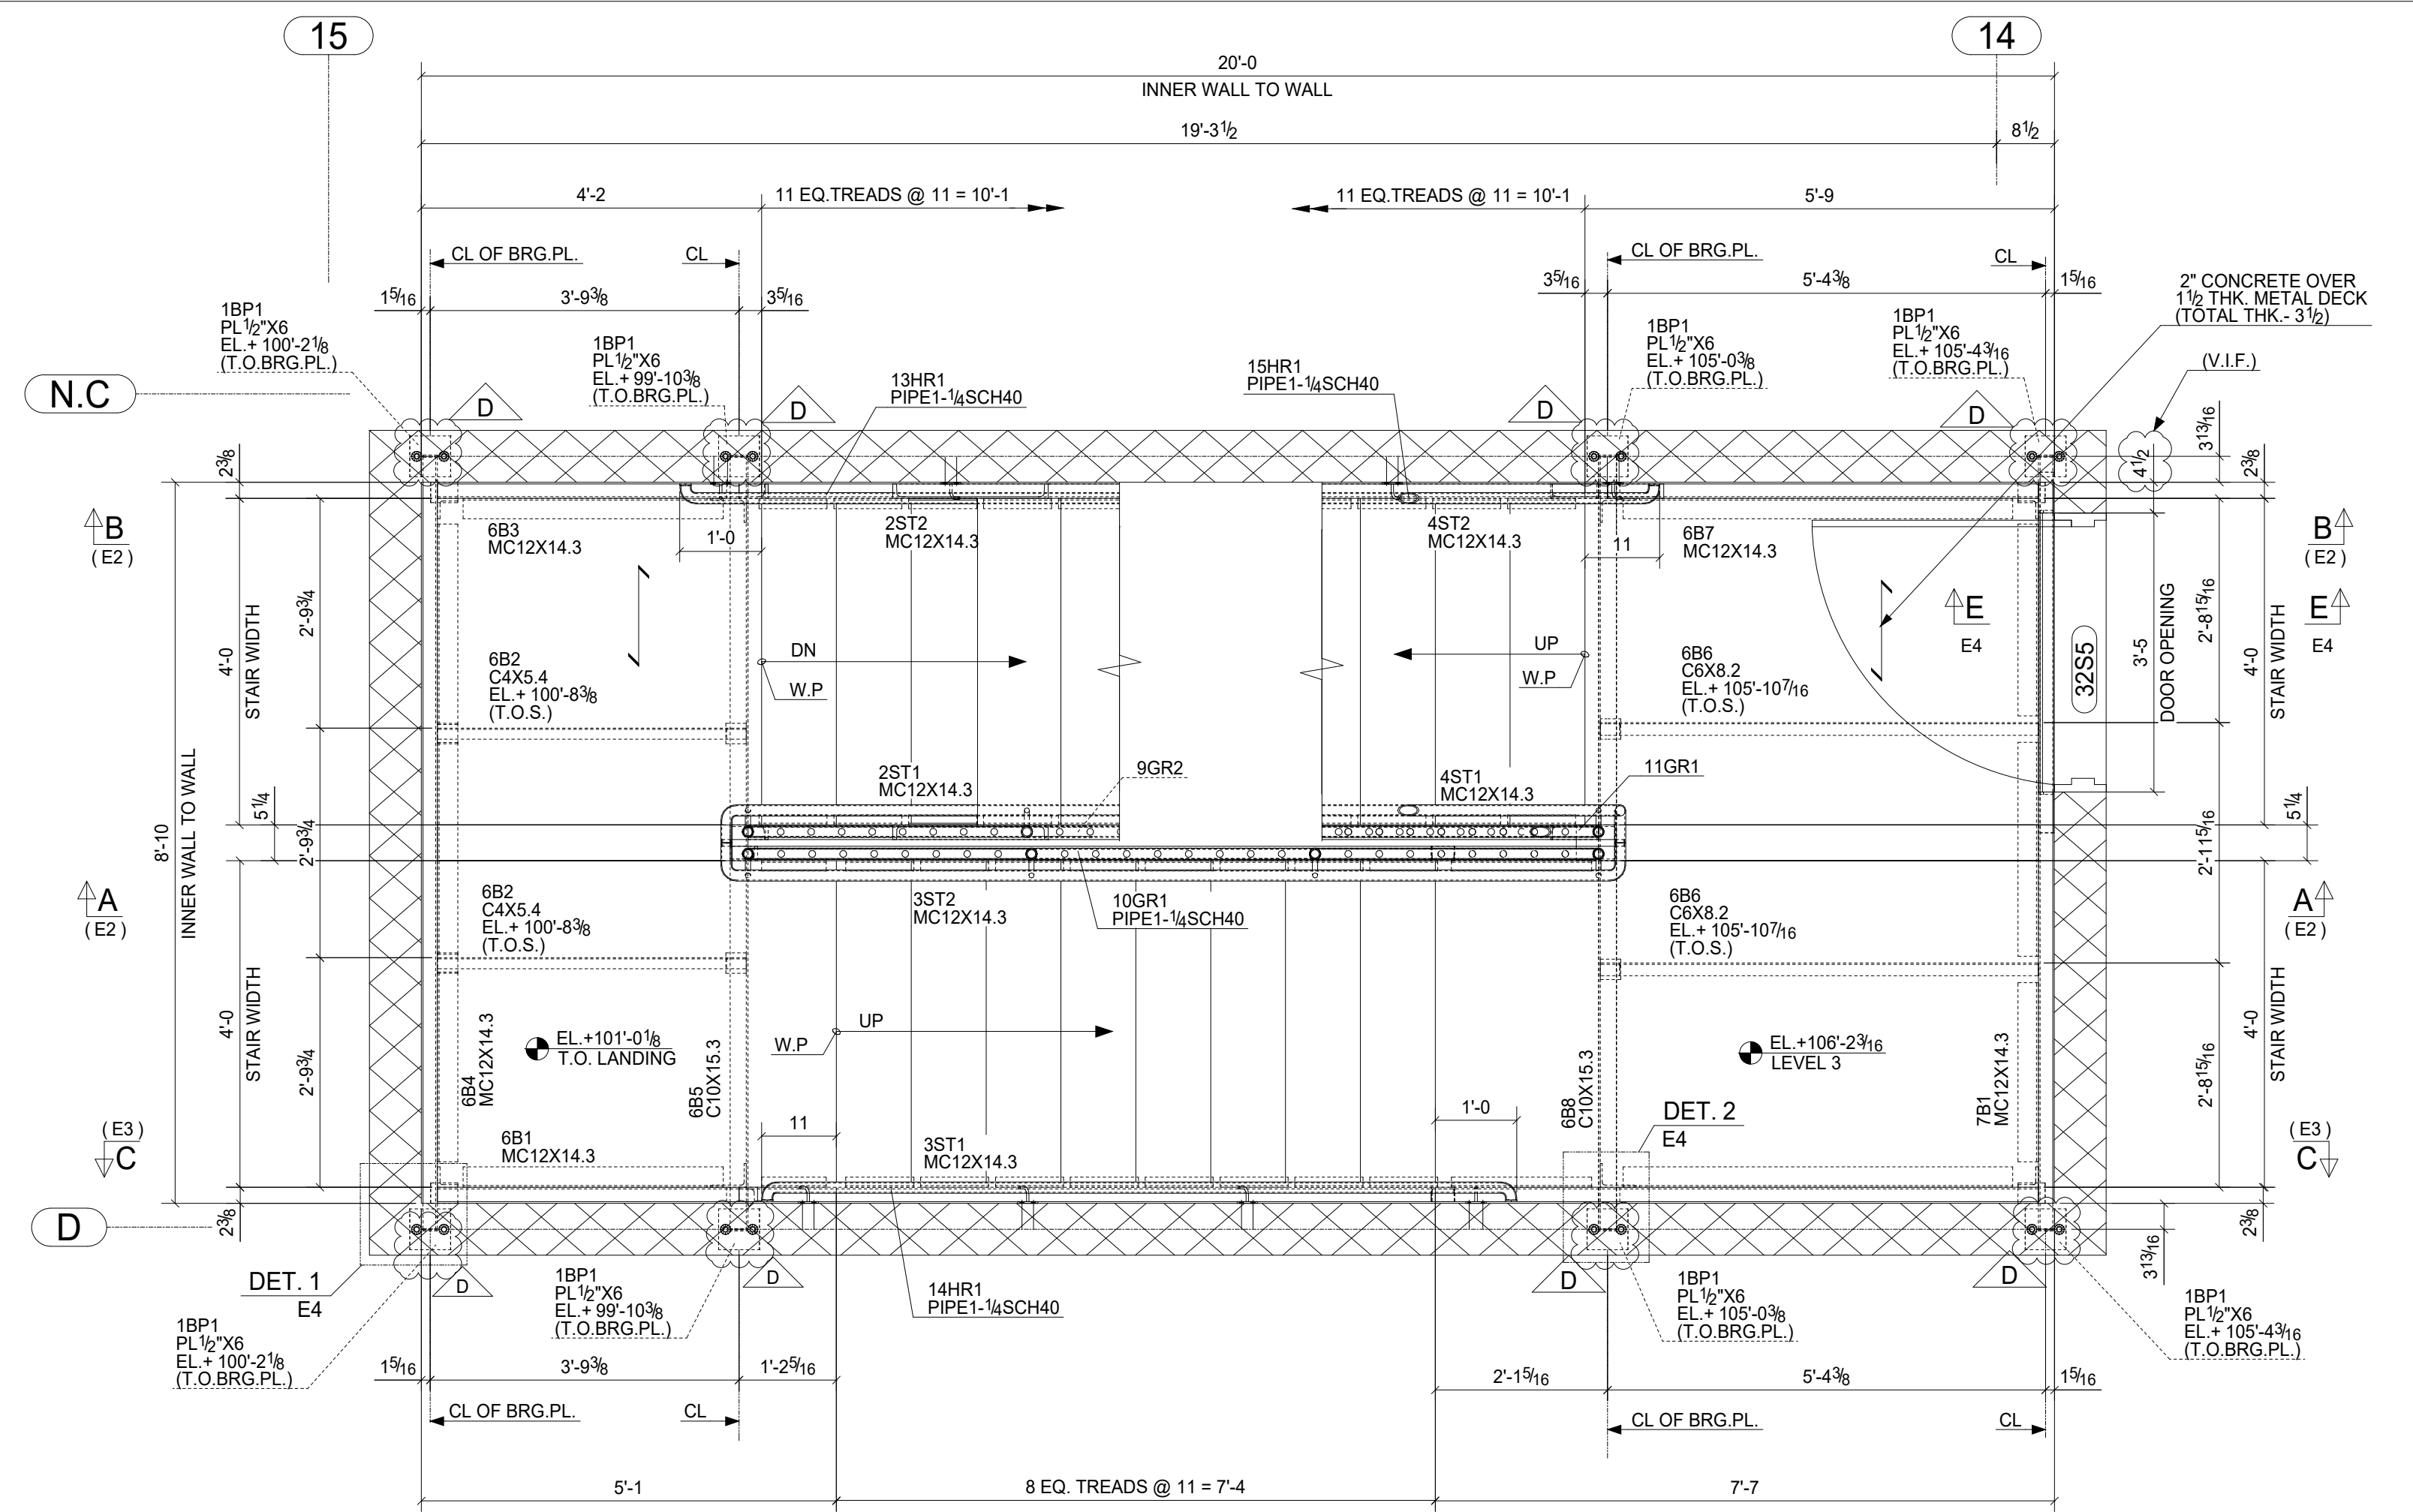

STAIR 1 MARKING PLAN AT LEVEL 2
(REF. CONTRACT DWG. NO. - 2/A0860)

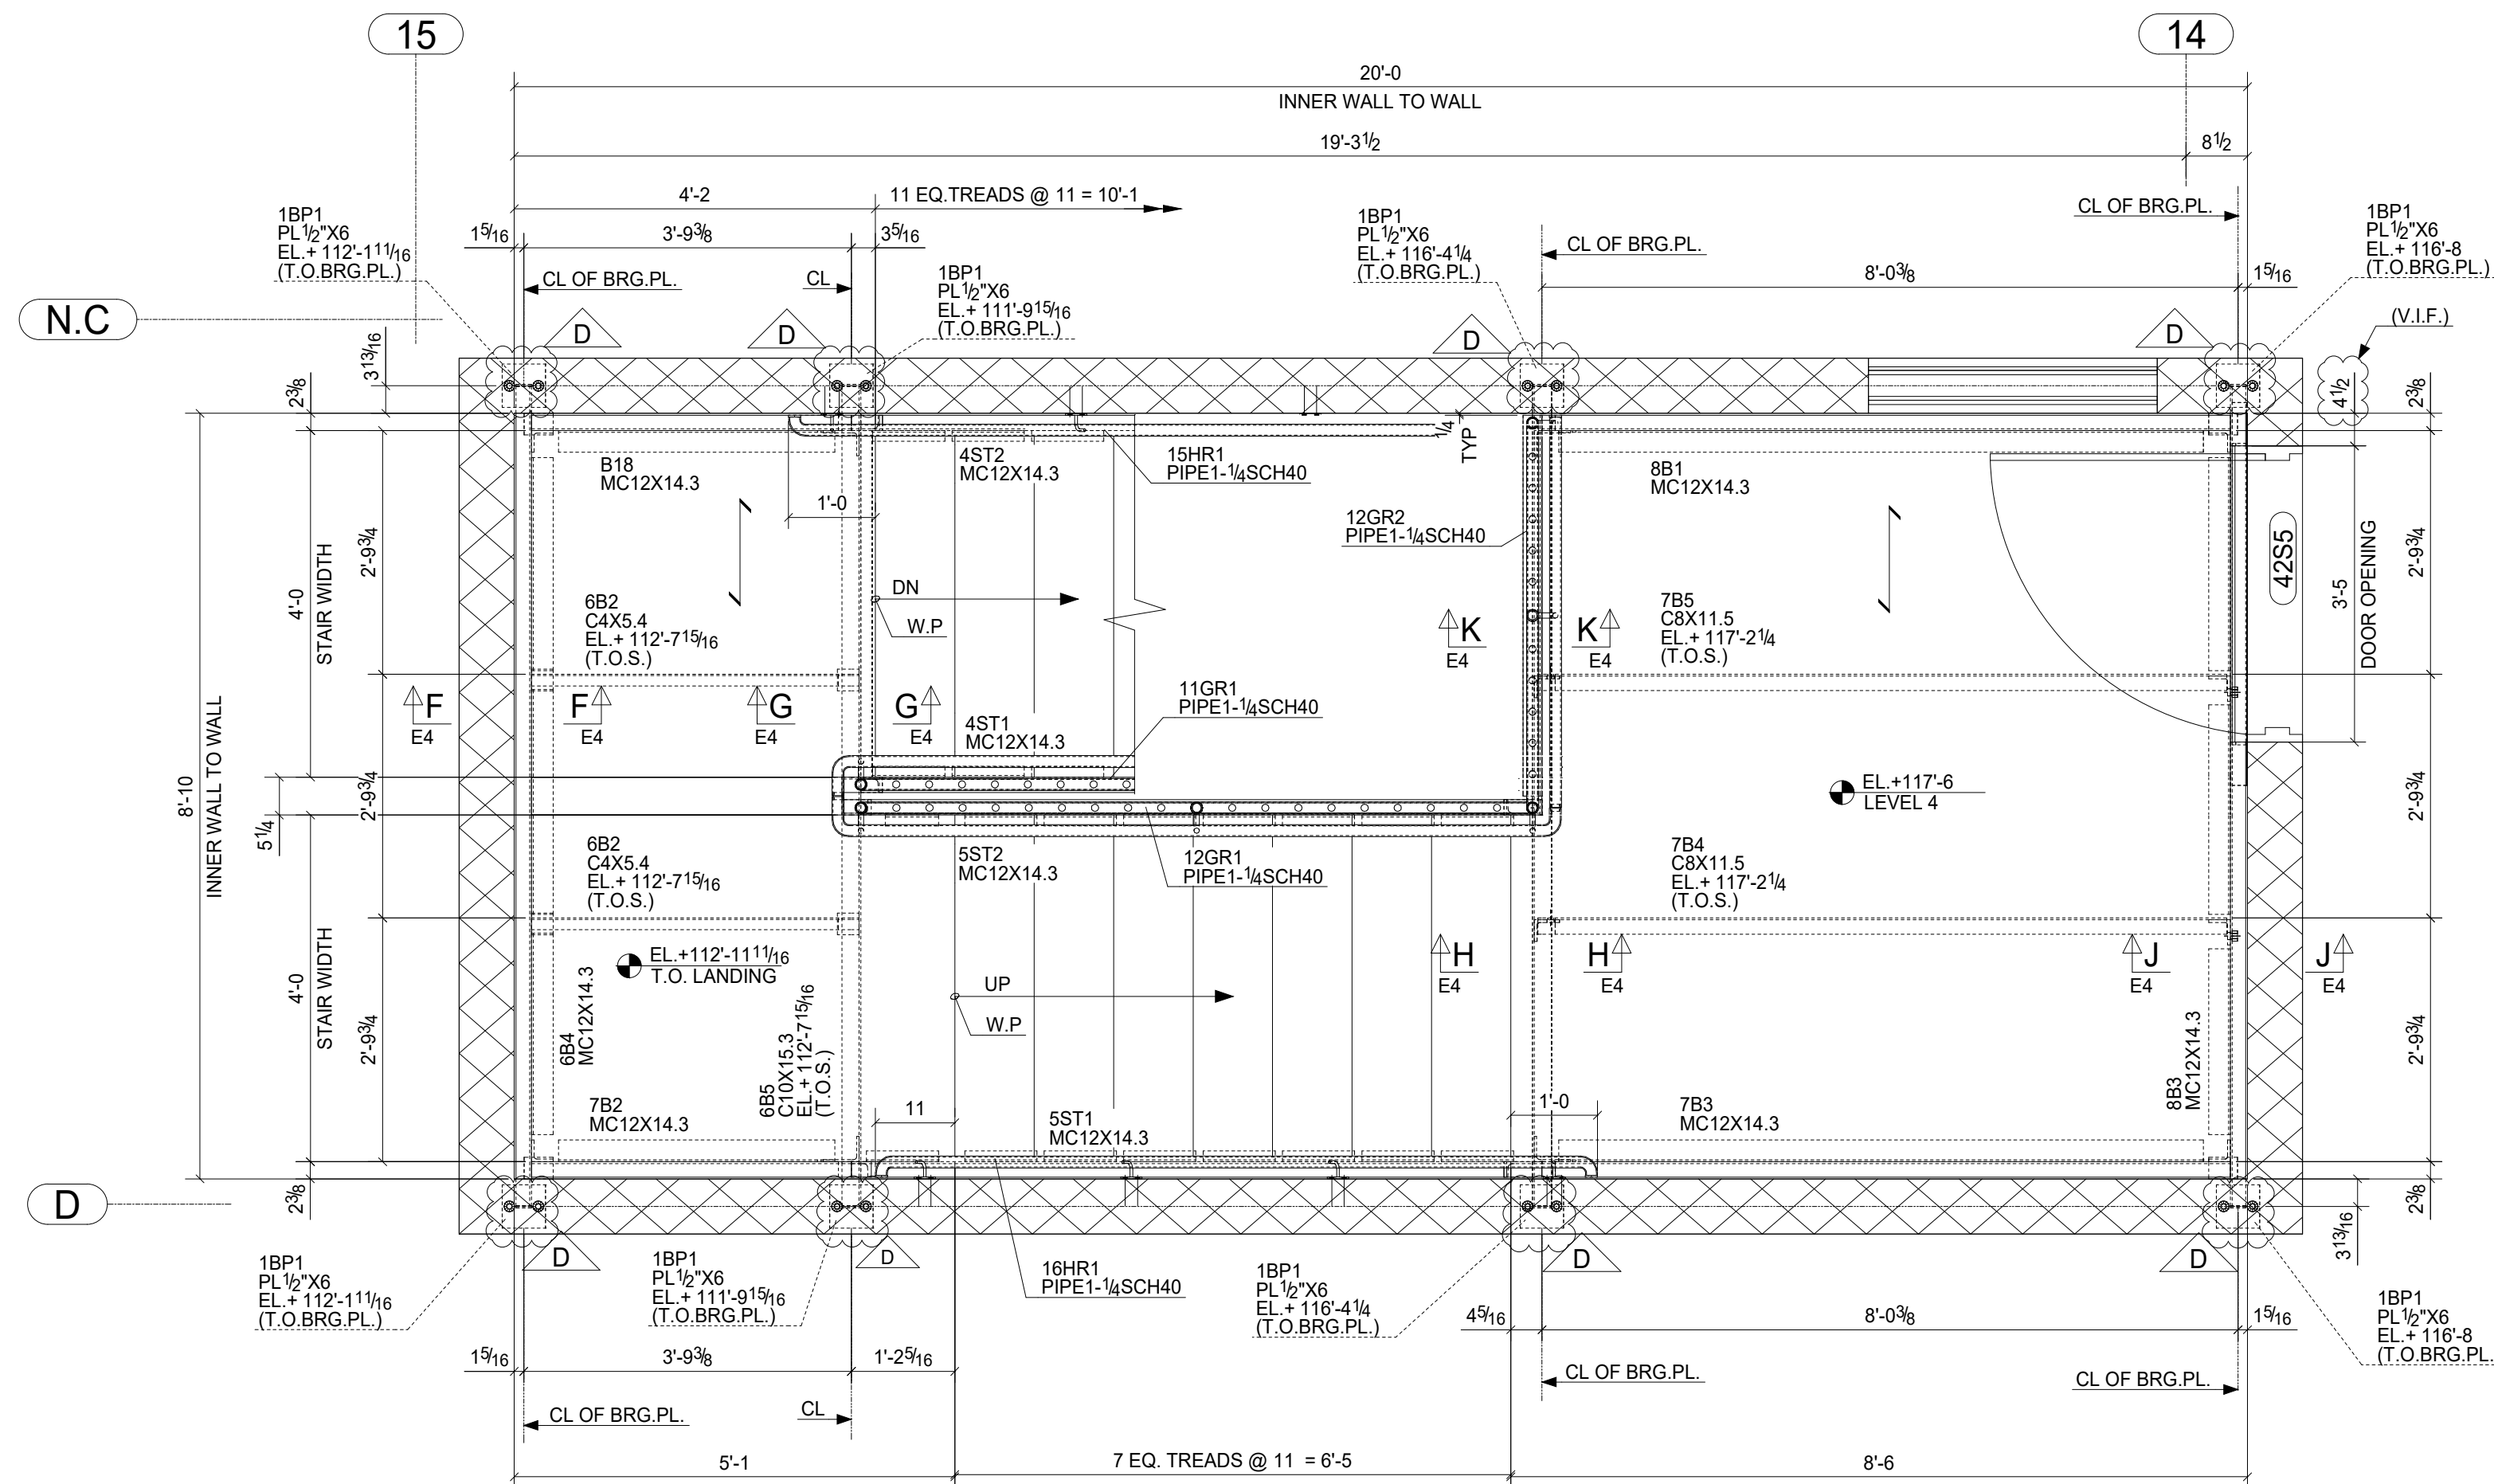

STAIR 11 MARKING PLAN AT LEVEL 3
(REF. CONTRACT DWG. NO. - 3/A0860)

NOTE:-

1) INDICATES DECK SPAN DIRECTION.